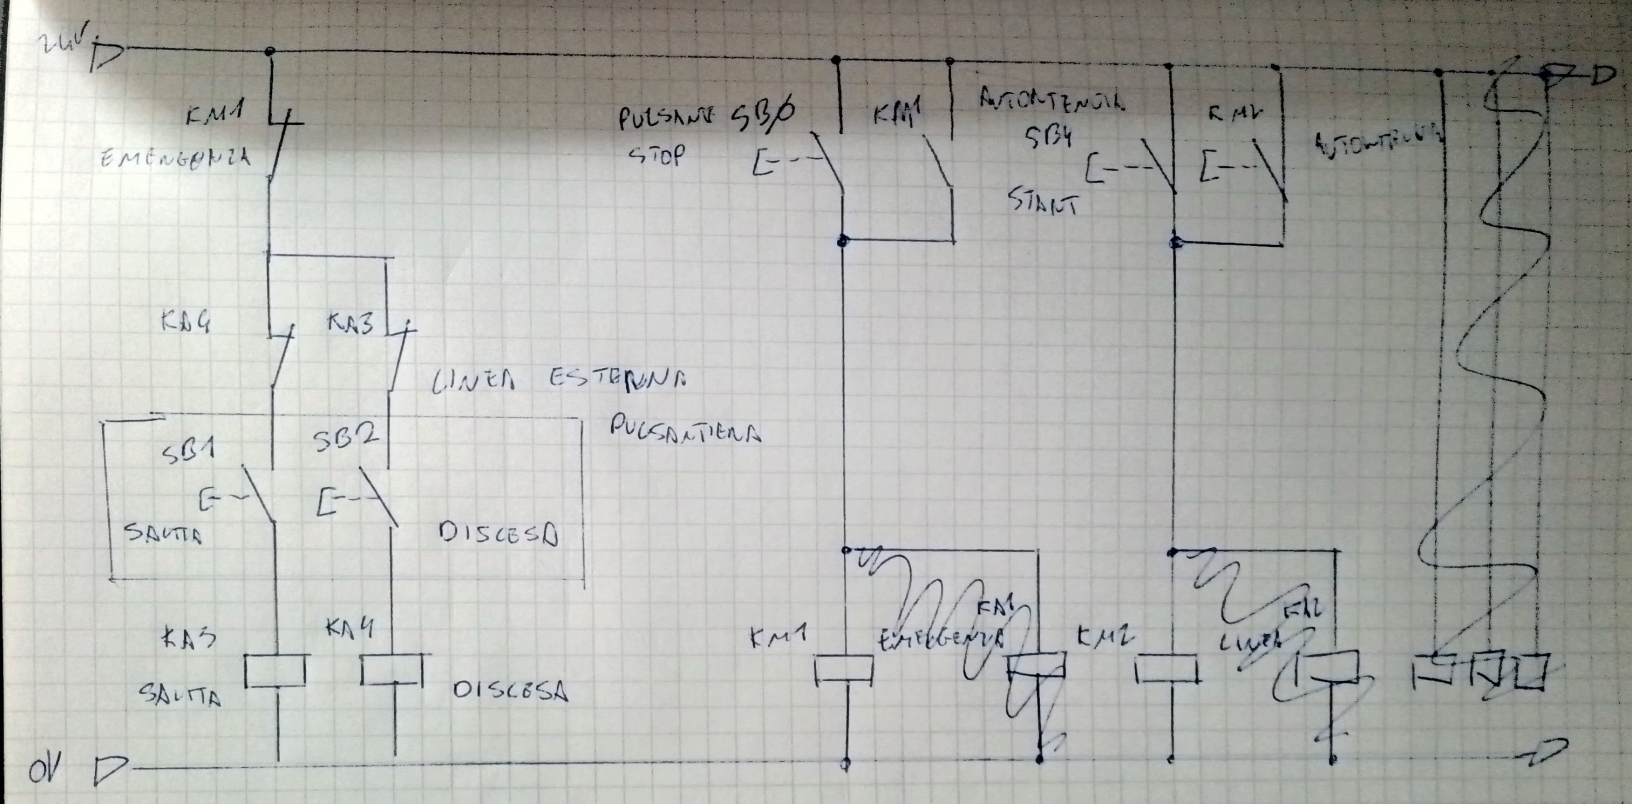
24V
KM1
EMERGENZA
PULSANTE SB0
STOP
KM1
AUTOTENUTA
SB4
START
KM1
AUTOTENUTA
KA4
KA3
LINEA ESTERNA
PULSANTIERA
SB1
SB2
SALITA
DISCESA
KA3
KA4
SALITA
DISCESA
KM1
EMERGENZA
KM1
KM2
LINEA
KM2
0V